


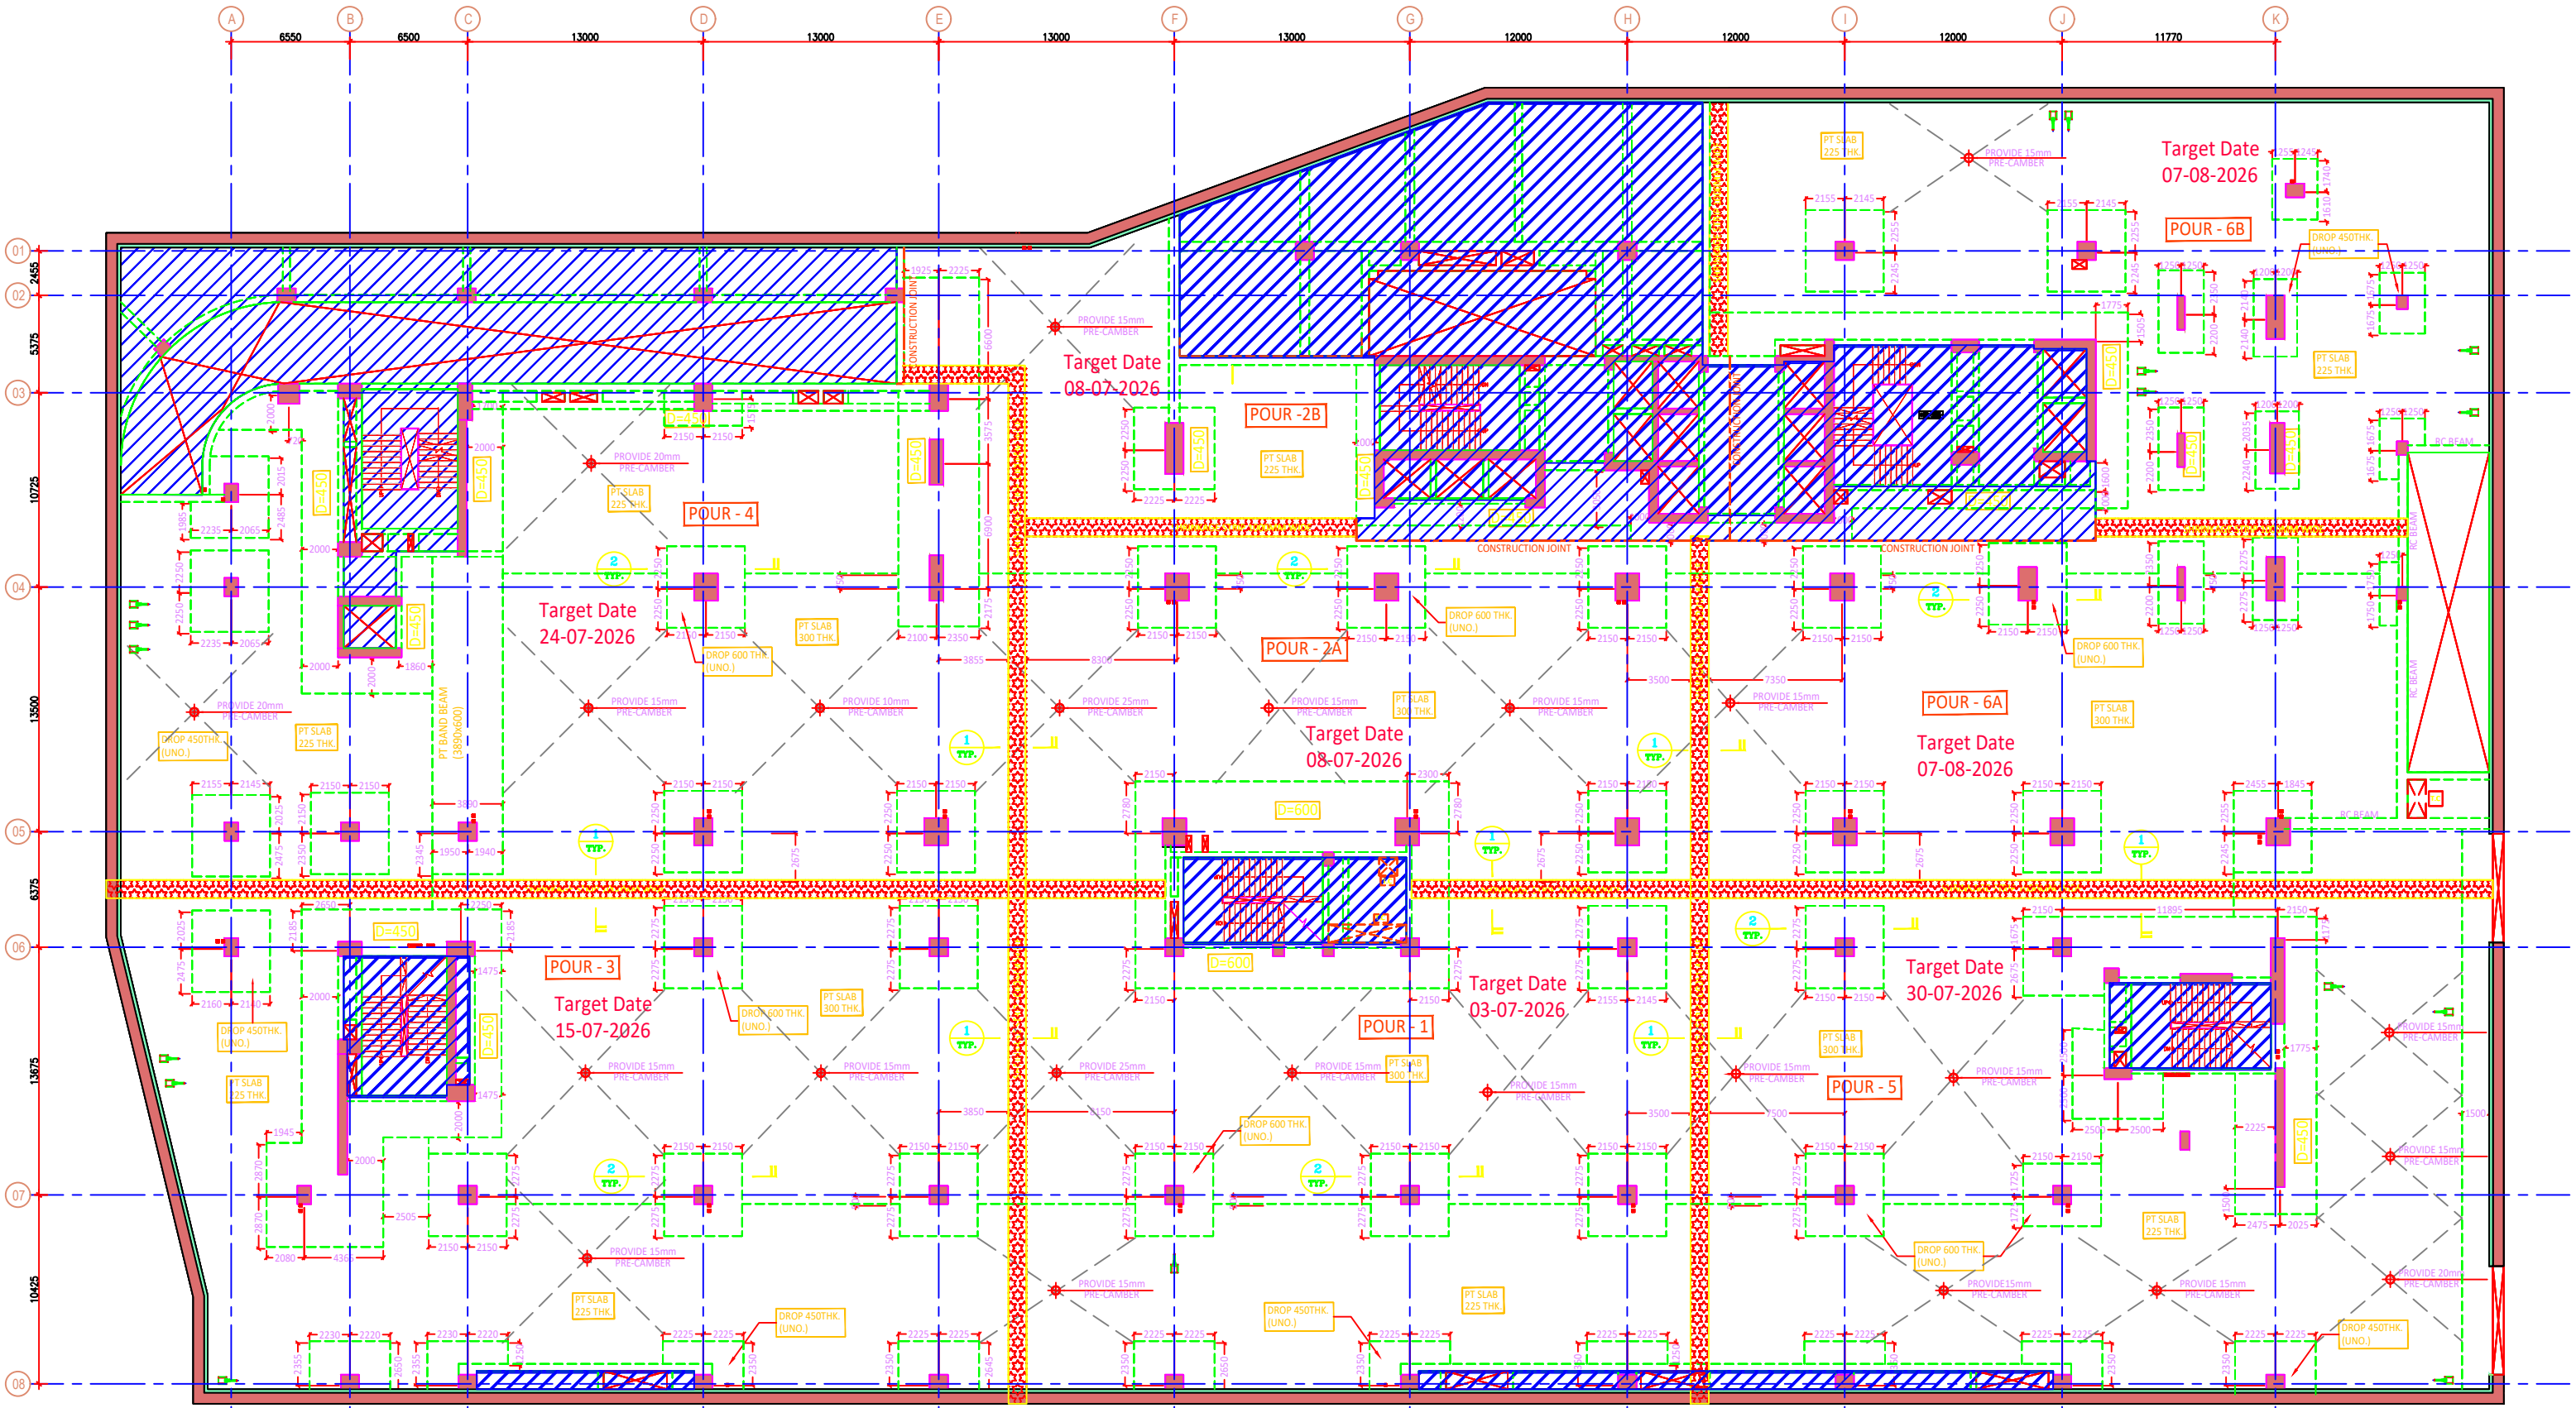

BASEMENT-2 FLOOR (TYPE 1) LEVEL
PT SLAB - FORMWORK LAYOUT PLAN

NOTE - TC - DENOTES TEMPORARY CUT-OUT FOR PT STRESSING

