


RAFT SEQUENCE

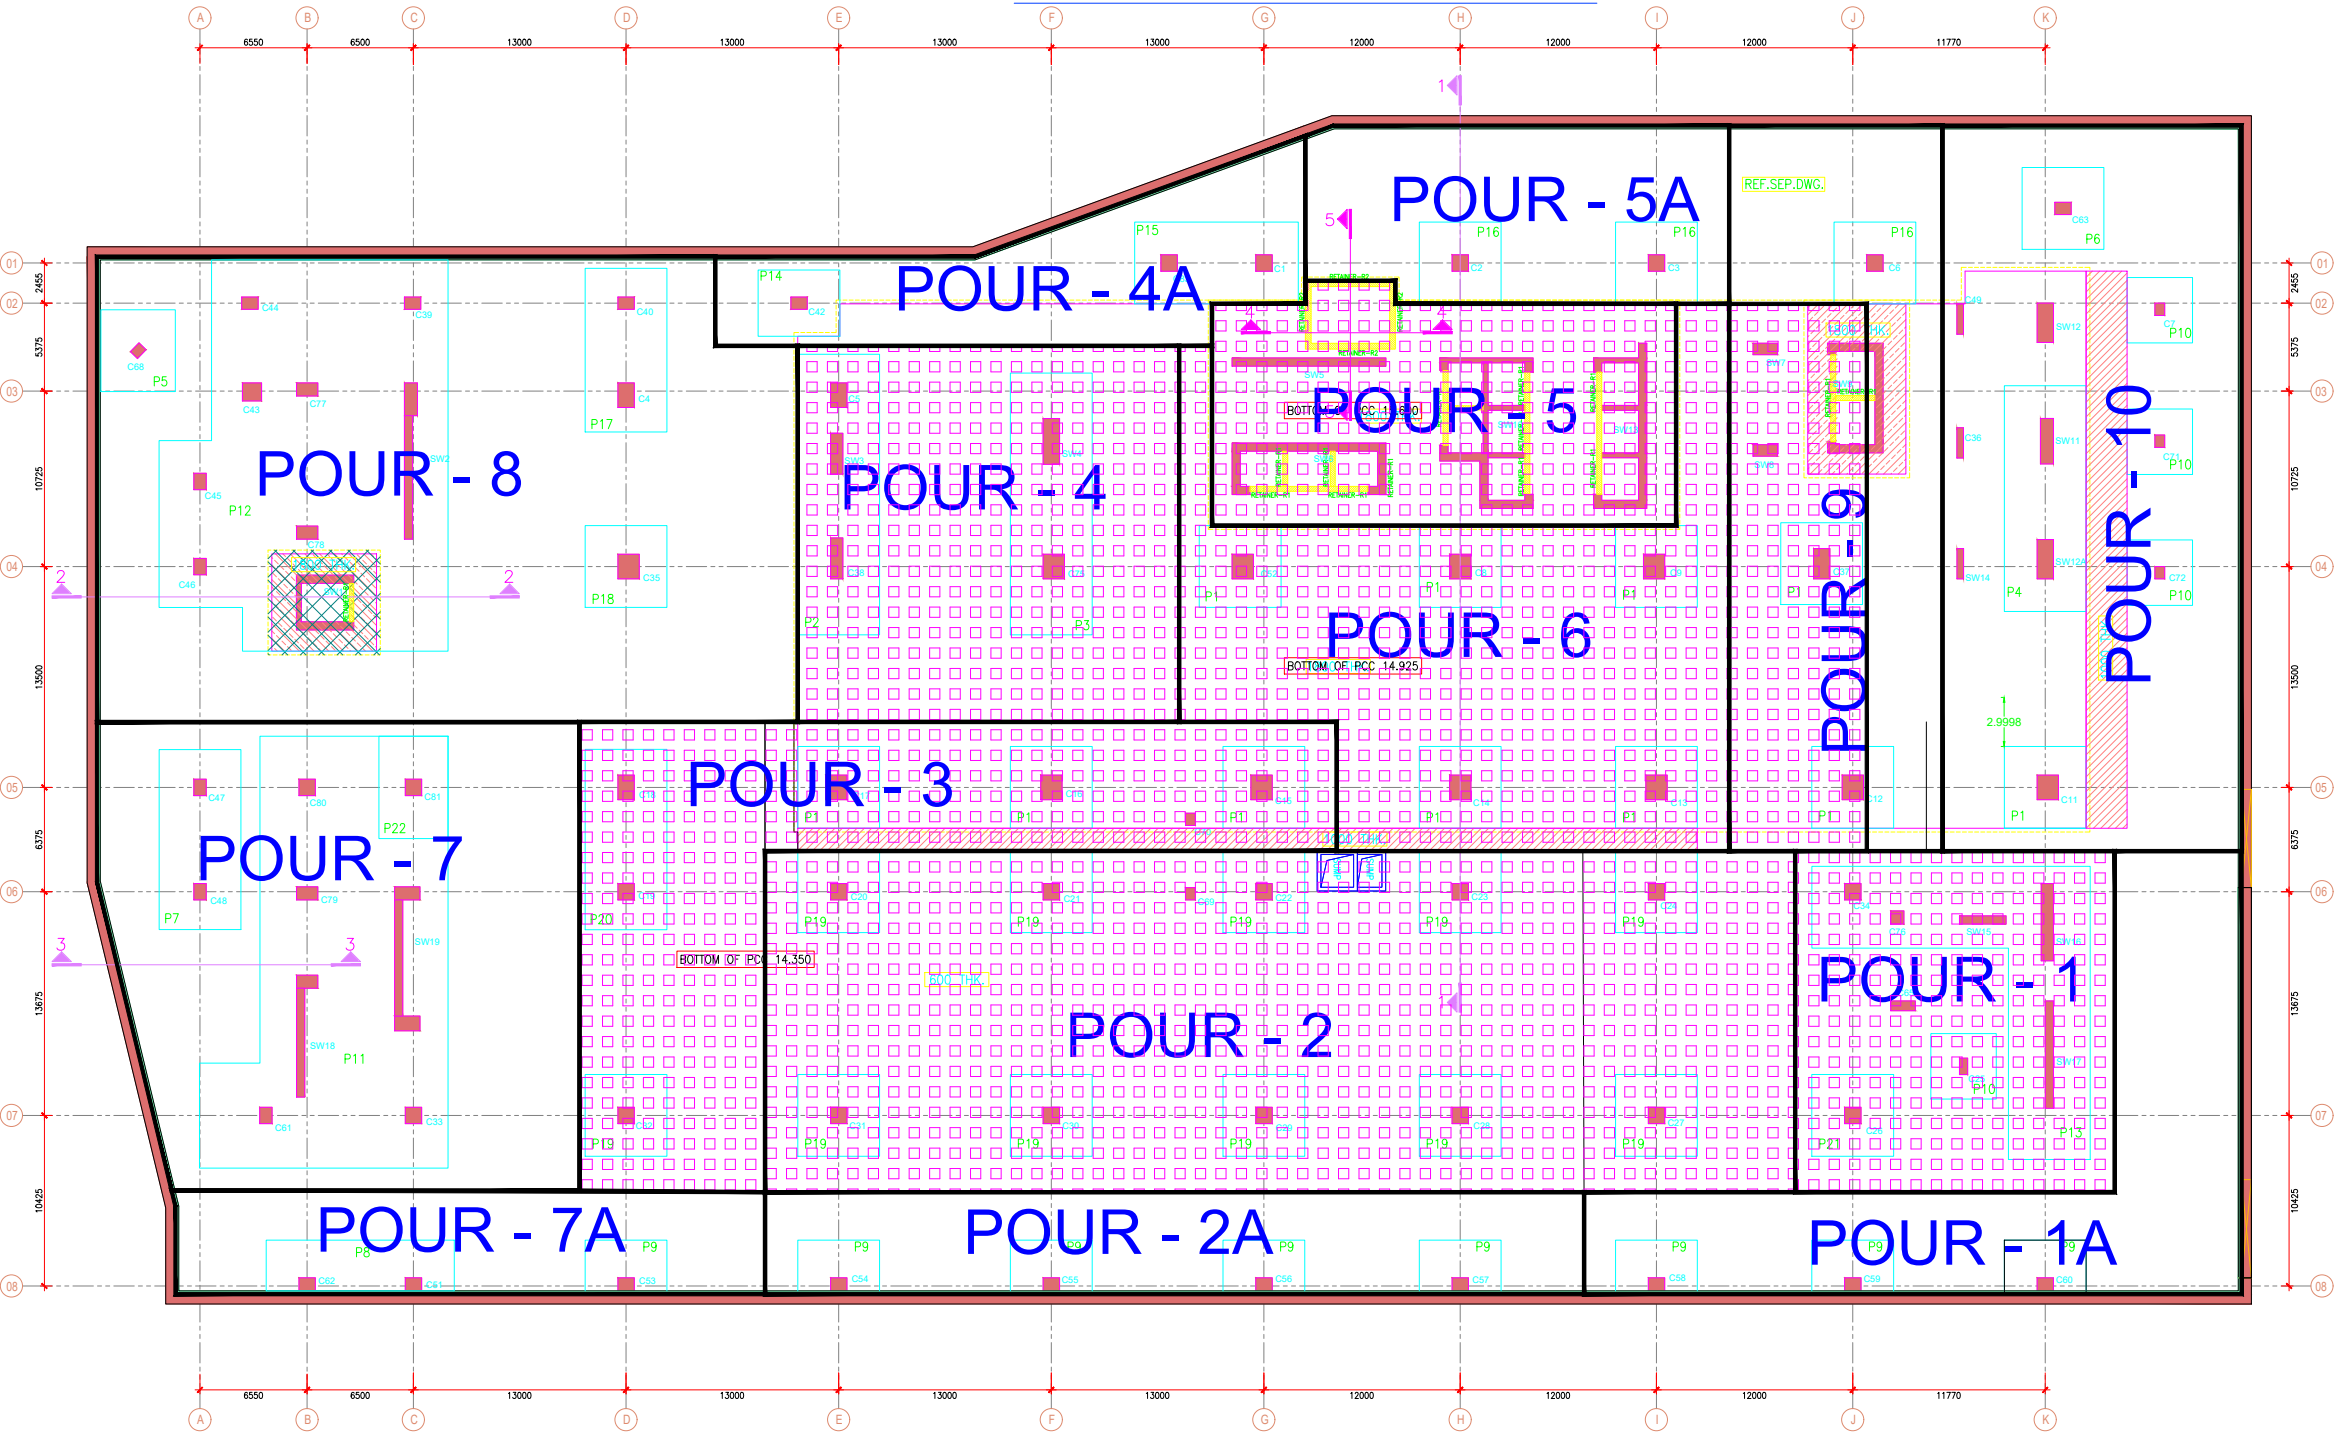

LEGEND		
	RAFT CASTED	4181 SQM
	POUR - 1A	412 SQM
	POUR - 2A	312 SQM
	POUR - 4A	257 SQM
	POUR - 5A	274 SQM
	POUR - 7	801 SQM
	POUR - 7A	227 SQM
	POUR - 8	1191 SQM
	POUR - 9	578 SQM
	POUR - 10	811 SQM